2026

portfólio *laís*

RENDERIZAÇÃO · MODELAGEM 3D · DETALHAMENTO · PROJETO EXECUTIVO

muito prazer!

Sou **Laís**, Designer Gráfico e estudante de Arquitetura e Urbanismo, atualmente cursando o 10º período. Desde muito nova, sou apaixonada pela arte de transformar espaços — sempre enxerguei na arquitetura e no design uma forma de dar vida às ideias, criar sensações e tornar ambientes memoráveis.

Atuo com terceirização de modelagem 3D, renderização, detalhamento e projeto executivo, atendendo arquitetos, designers e construtoras. Meu foco é entregar imagens e materiais técnicos que comuniquem com clareza, qualidade e sensibilidade cada projeto.

BACHAREL EM DESIGN GRÁFICO
cursando Arquitetura e Urbanismo — 10º período

MÚLTIPLOS CURSOS
renderização — modelagem — detalhamento

EXPERIÊNCIA PRÁTICA EM ESCRITÓRIO
estágio de 2 anos + freelancer em andamento

RENDERIZAÇÃO · MODELAGEM 3D · DETALHAMENTO · PROJETO EXECUTIVO · PERSONALIZAÇÃO DE DOCUMENTOS

5+
anos de experiência na área do design gráfico

150+
imagens no portfólio

8+
softwares dominados

324h
de cursos de especialização

POR QUE *terceirizar* COMIGO

você projeta, eu produzo
assumo a produção técnica e visual para você ganhar tempo e focar no que importa: criar e atender seus clientes.

V-Ray e IA no mesmo fluxo
fotorrealismo tradicional quando o detalhe pede, renderização com IA quando o prazo pede — a melhor ferramenta para cada entrega.

olhar de designer
organização visual, composição e cuidado com a apresentação em cada imagem, prancha e documento.

entrega pronta para usar
arquivos finalizados para apresentar ao cliente, levar para a obra ou entregar à banca.

PORTFÓLIO DE *renders*

uma seleção de imagens produzidas pra escritórios de arquitetura, designers e projetos autorais — em V-Ray e com renderização por IA.

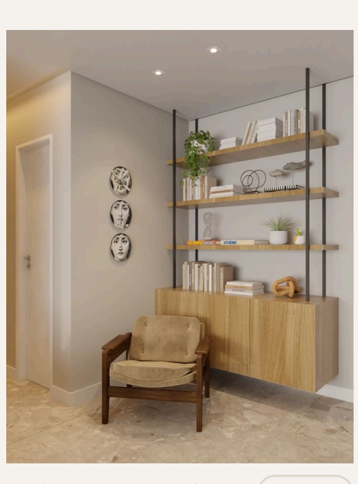
Projeto: Barlô Arquitet... V-RAY

Projeto: Barlô Arquitet... V-RAY

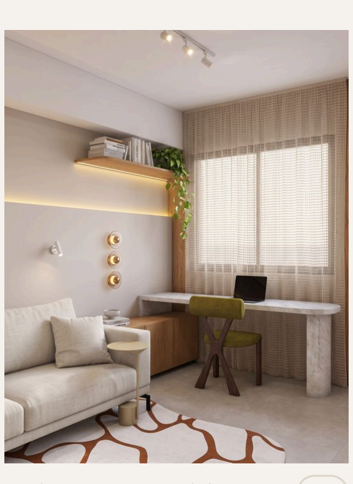
Projeto: Natasha Vieira IA

Projeto: Barlô Arquitet... V-RAY

Projeto: Barlô Arquitet... V-RAY

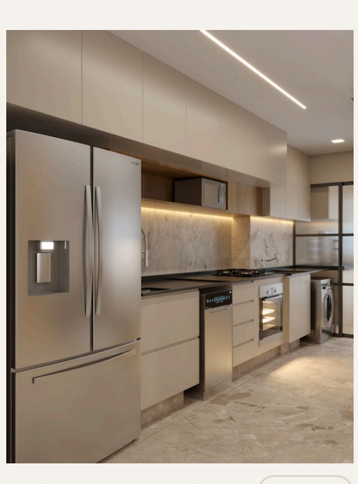
Projeto: Barlô Arquitet... V-RAY

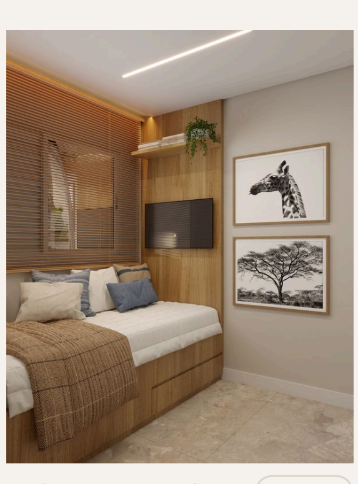
Projeto: Barlô Arquitet... V-RAY

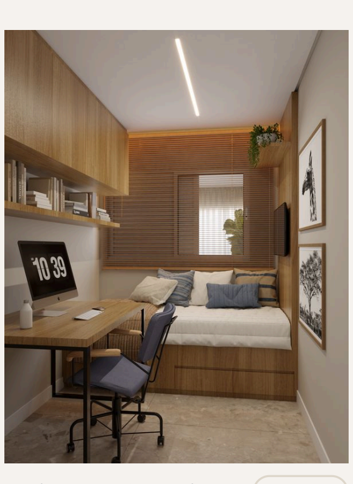
Projeto: Barlô Arquitet... V-RAY

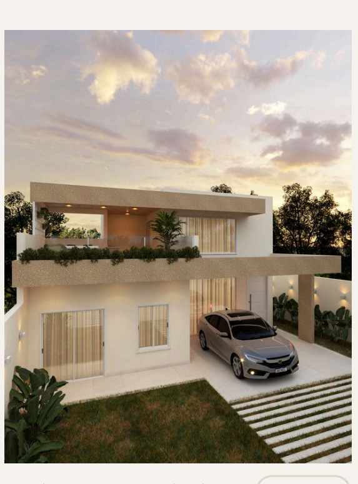
Projeto: Lucas Oliveira V-RAY

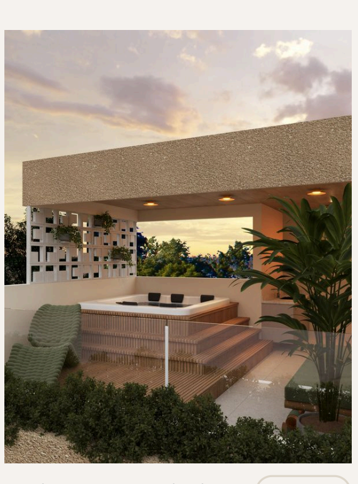
Projeto: Lucas Oliveira V-RAY

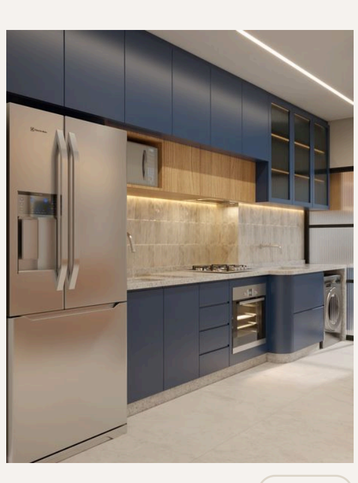
Projeto: Laís Vieira V-RAY

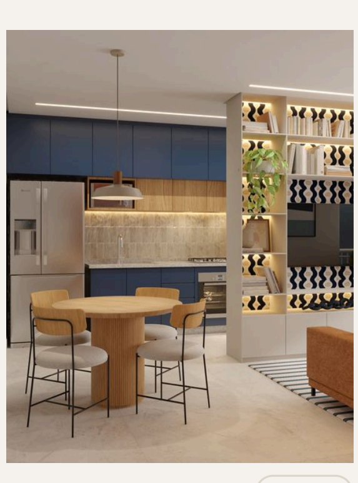
Projeto: Laís Vieira V-RAY

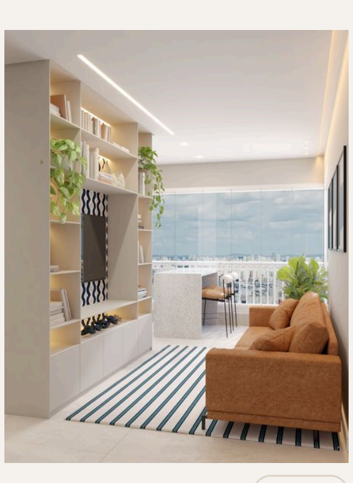
Projeto: Laís Vieira V-RAY

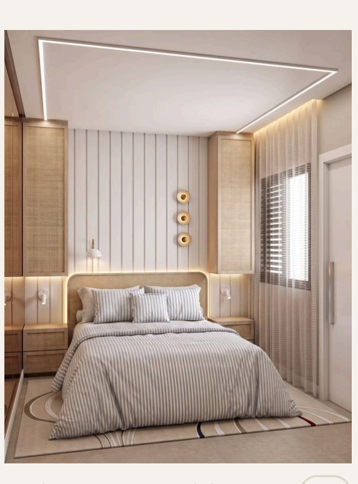
Projeto: Natasha Vieira IA

Projeto: Laís Vieira V-RAY

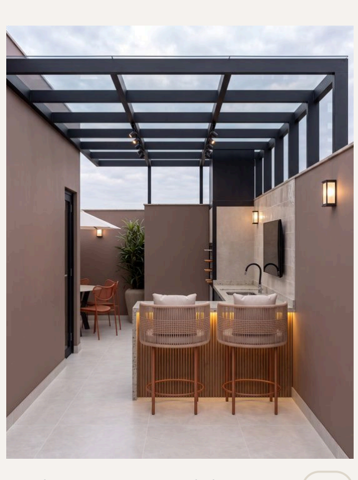
Projeto: Natasha Vieira IA

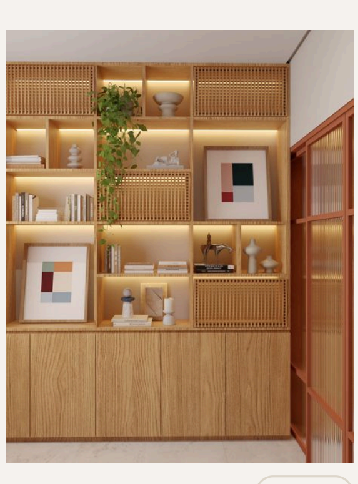
Projeto: Laís Vieira V-RAY

Projeto: Laís Vieira V-RAY

Projeto: Laís Vieira V-RAY

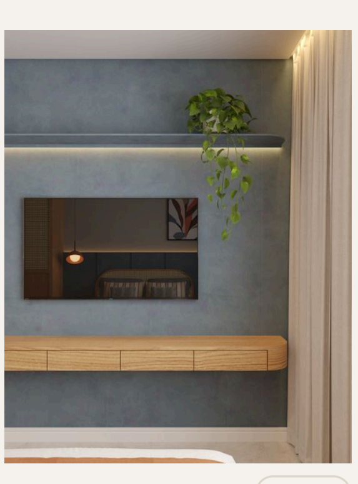
Projeto: Laís Vieira V-RAY

Projeto: Morada IA

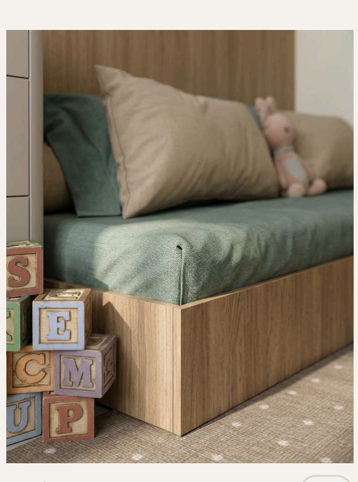
Projeto: Morada IA

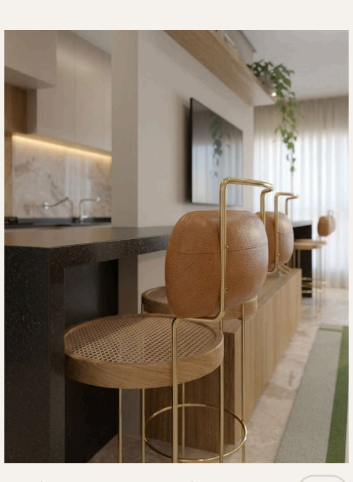
Projeto: Barlô Arquitetura IA

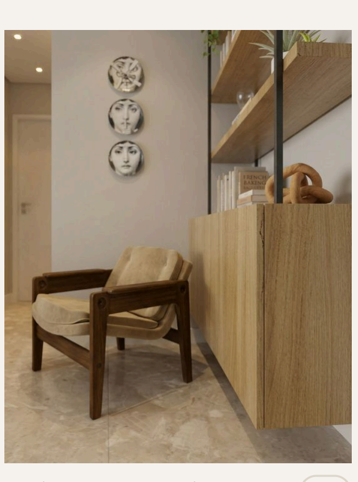
Projeto: Barlô Arquitetura IA

Projeto: Natasha Vieira IA

Projeto: Marla Riva IA

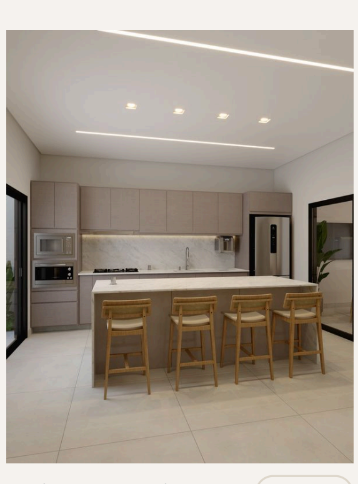
Projeto: Marla Riva V-RAY

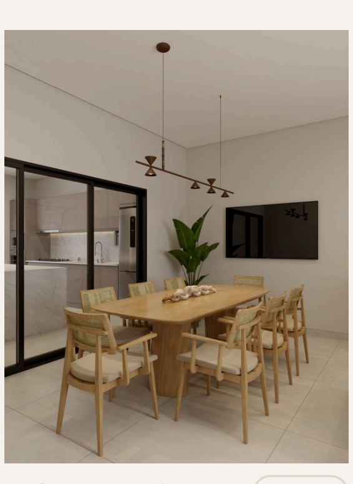
Projeto: Marla Riva V-RAY

Projeto: Marla Riva V-RAY

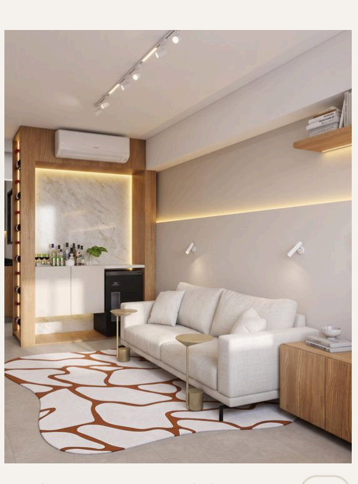
Projeto: Natasha Vieira IA

PLANTA BAIXA *humanizada*

PROJETO
Letícia Guedes

MODELAGEM
Laís A. Vieira

SOFTWARE UTILIZADO
Sketchup · IA

A planta baixa humanizada facilita a compreensão do projeto ao torná-lo mais visual e realista, ajudando o cliente a entender melhor o espaço e tomar decisões com mais segurança. Além disso, melhora a comunicação e valoriza a apresentação.

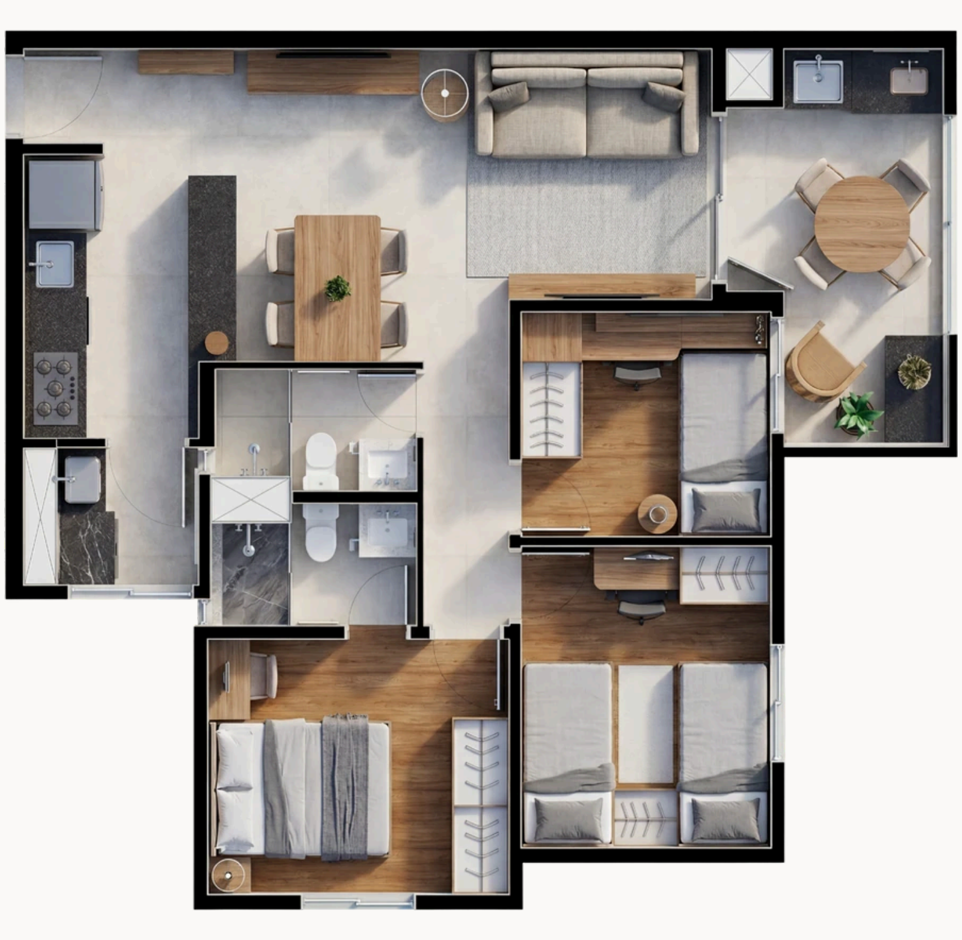

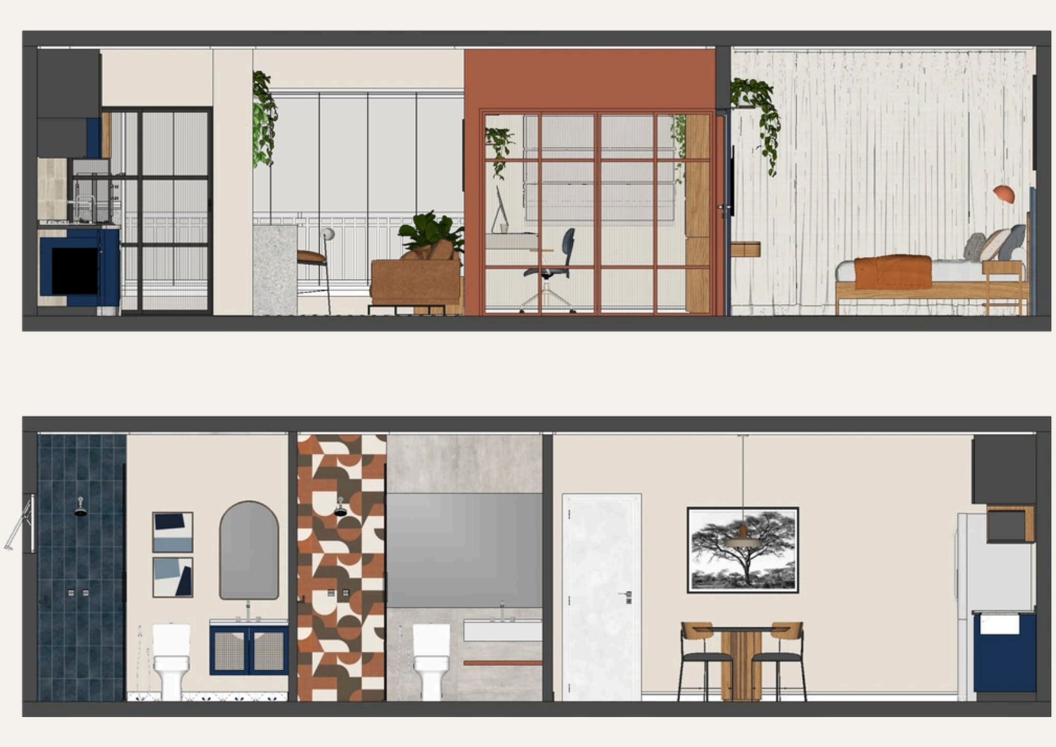

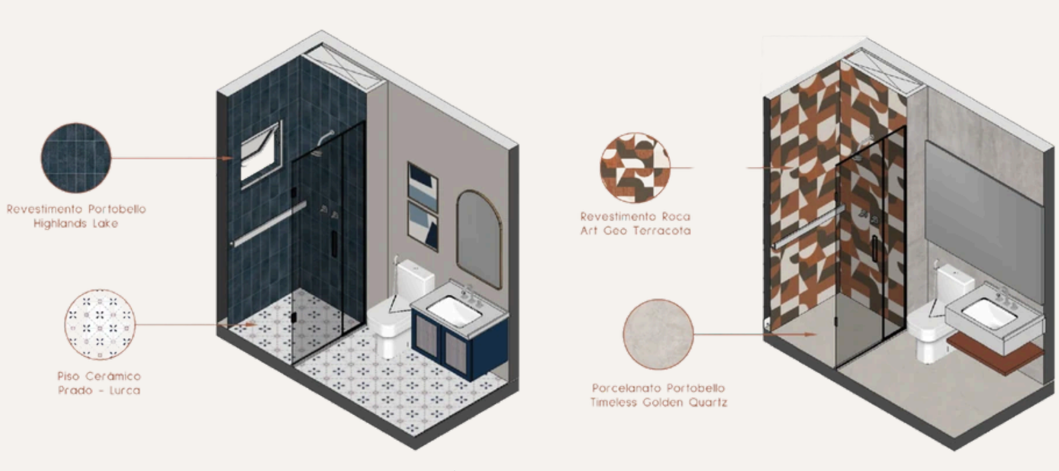
Revestimento Portobello Highlands Lake
Piso Cerâmico Prado - Lurca
Revestimento Roca Art Geo Terracota
Porcelanato Portobello Timeless Golden Quartz

isométricas humanizadas

CORTE *humanizado*

PROJETO
Laís A. Vieira

MODELAGEM
Laís A. Vieira

SOFTWARE UTILIZADO
Sketchup · Layout

Cortes e isométricas humanizadas tornam o projeto mais claro e didático, mostrando alturas, volumes e profundidade de forma visual e realista. Eles ajudam a entender melhor o espaço, enxergar detalhes construtivos e se conectar com o projeto com mais facilidade.

DO CONCEITO À *execução*

PROJETO
Prazark Arquitetura

DETALHAMENTO
Laís A. Vieira

SOFTWARE UTILIZADO
Sketchup · Layout

O projeto executivo é essencial para transformar a ideia em obra, reunindo todos os detalhamentos técnicos necessários para a execução correta. Ele garante clareza para os profissionais, evita erros e retrabalhos, e assegura que o resultado final siga exatamente o que foi planejado.

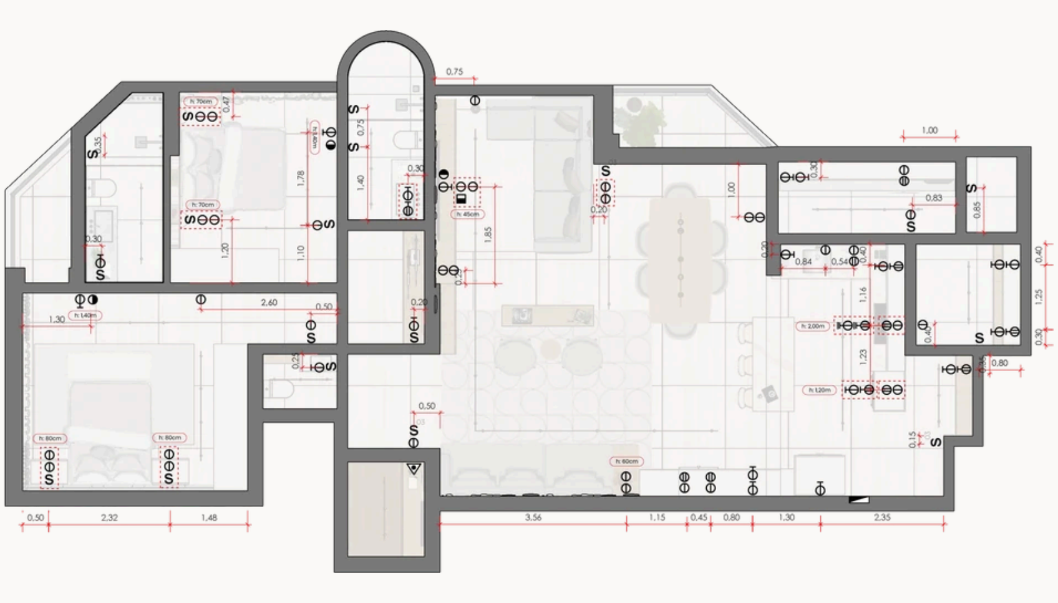

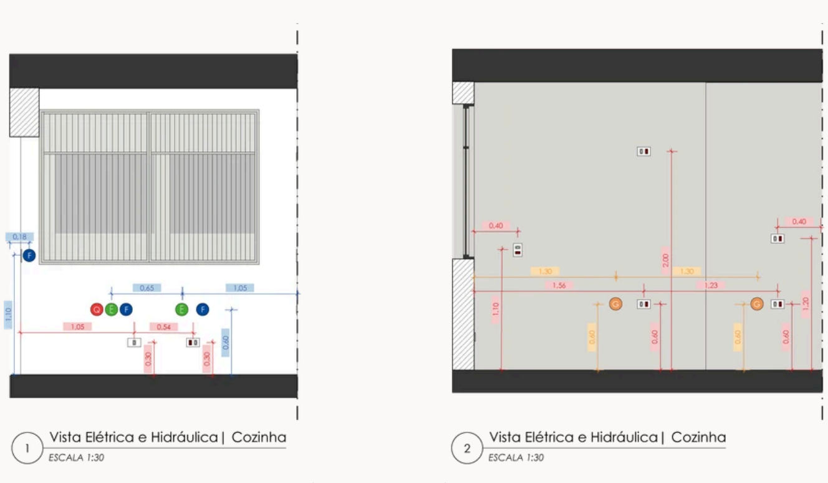
1 Vista Elétrica e Hidráulica | Cozinha
ESCALA 1:30
2 Vista Elétrica e Hidráulica | Cozinha
ESCALA 1:30

vistas elétrica e hidráulica — cozinha

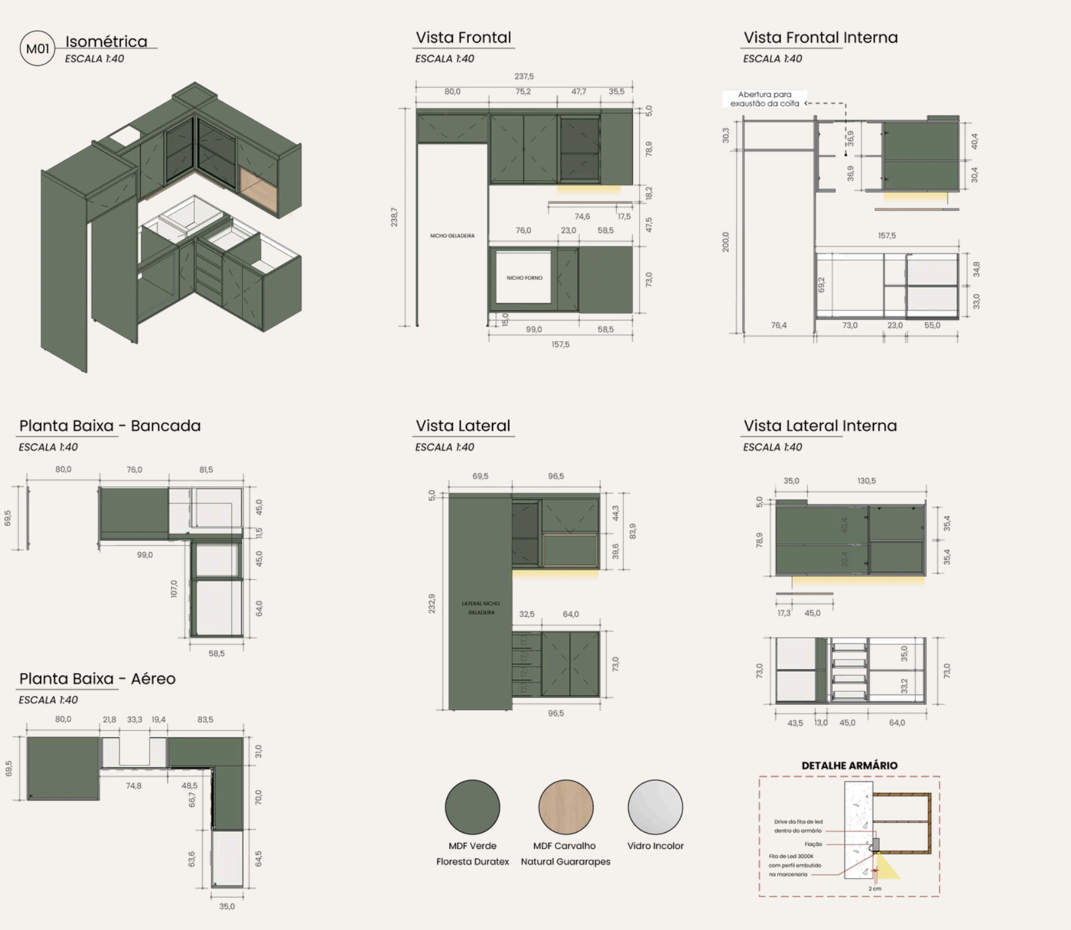

PRECISÃO EM CADA *detalhe*

PROJETO
Daniele Rossi

DETALHAMENTO
Laís A. Vieira

SOFTWARE UTILIZADO
Sketchup · Layout

O detalhamento de marcenaria, serralheria, marmoraria ou outro garante que cada elemento seja executado com precisão, definindo medidas, materiais e acabamentos. Ele evita erros na produção, facilita a comunicação com os fornecedores e assegura um resultado final fiel ao projeto.

IDEIAS QUE GANHAM *forma*

PROJETO
Barlô Arquitetura

MODELAGEM
Laís A. Vieira

SOFTWARE UTILIZADO
Sketchup

A modelagem 3D é a etapa em que as ideias e o projeto começam a ganhar forma. Ela permite que o cliente visualize os espaços antes da execução da obra, facilitando o entendimento do projeto, a tomada de decisões e a identificação de possíveis ajustes ainda na fase de planejamento.

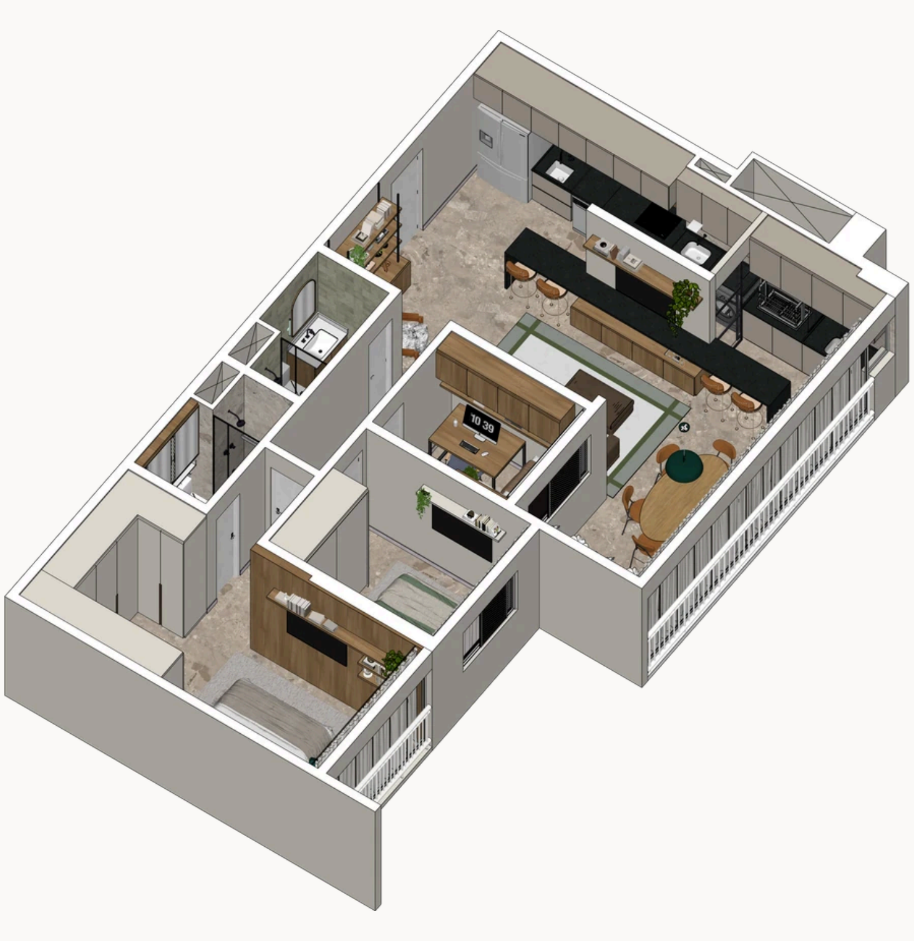

COMO *funciona*

01
briefing
você me manda os arquivos, referências e o que precisa pro seu projeto.

02
ajustes
faço os possíveis ajustes necessários no arquivo recebido antes de começar.

03
execução
desenvolvo o serviço combinado — render, modelagem, detalhamento ou diagramação.

04
entrega final
você recebe os arquivos prontos pra apresentar — ao cliente, à obra ou à banca.

CURSOS E *softwares*

10 cursos · 324h de formação em renderização, modelagem e detalhamento.

PROJETO RENDER PLACE AC Renderiza	100h	
V-RAY LIGHTS ON AC Renderiza	40h	
FOTORREALISMO EM CENAS INTERNAS COM V-RAY AC Renderiza	8h	
PRIA — RENDERIZAÇÃO COM IA Larissa Kiefer	20h	
FOTORREALISMO EM CENAS EXTERNAS COM V-RAY Chahoud	8h	
IA RENDER — RENDERIZAÇÃO COM IA AC Renderiza	22h	
BMAP — LAYOUT DO SKETCHUP Studio Baroli	60h	
IA.CLASS CLUB — RENDERIZAÇÃO COM IA Leticia de Paula	10h	
BMAM — LAYOUT E SKETCHUP PARA MARCENARIA Studio Baroli	50h	
SKETCHUP E LUMION Lucas Xavier	6h	

AutoCAD · SketchUp · Layout · Vectorworks · Illustrator · Photoshop · V-Ray · Canva · IA

obrigada!

cada projeto tem uma história — vou adorar ajudar a contar a sua. chame no WhatsApp para conversarmos sobre o seu projeto e receber um orçamento.

FALAR NO WHATSAPP

E-MAIL
arq.laisav@gmail.com

WHATSAPP
+55 11 96928-8192

INSTAGRAM
@lais_3d

SITE
www.lais3d.com.br

aponte a câmera para o WhatsApp